



---

**PRISCILA**

EXECUTIVO - COZINHA



CLIENTE: **PRISCILA**

AMBIENTE: **Cozinha**

PROJETISTA TÉCNICO: **JOÃO FELIPE SANTOS**

ARQUITETA: **FERNANDA**

**ATENÇÃO:**

DECLARO ESTAR DE ACORDO COM ESTE PROJETO E COM AS MEDIDAS NELE DESCRITAS E CIENTE DE QUE NELE CONSTAM APENAS PEÇAS E MÓDULOS DA EMPRESA, SENDO QUE OS DEMAIS ITENS SÃO MERAMENTE ILUSTRATIVOS (TAIS COMO ELETROS, COLCHÕES, GRANITOS E DECORAÇÕES NO GERAL).

ASS: \_\_\_\_\_

**PRANCHA  
02**

## **CONTRATO**

### **LEIA COM ATENÇÃO**

**1-** CLIENTE ESTÁ RECEBENDO UMA CÓPIA DOS PROJETOS ADQUIRIDOS E ESTÁ DE ACORDO COM AS INFORMAÇÕES APONTADAS SOBRE MODELO, COR, ACABAMENTO, ESTRUTURAS, ACESSÓRIOS E CONDIÇÕES QUE FAZEM PARTE DESTES PROJETOS EXECUTIVOS.

**2-** O MESMO FOI ELABORADO CONSIDERANDO AS MEDIDAS REAIS DESTES AMBIENTES, SE HOUVER ALGUMA ALTERAÇÃO NO PÉ DIREITO OU NAS PAREDES, REFERENTE À INSTALAÇÃO DE MOLDURAS DE GESSO, RODAPÉS, MODIFICAÇÃO EM INSTALAÇÃO DA MODULAÇÃO NO DIA DA MONTAGEM, A EMPRESA NÃO SE RESPONSABILIZA QUANTO A FUTUROS CONTRATEMPOS DEVIDOS ÀS ALTERAÇÕES. CABE AO CLIENTE AVISAR O PROJETISTA ANTES DA MEDIÇÃO FINAL PARA ADEQUAÇÃO DA MODULAÇÃO.

**3-** SE HOUVER GRANITO NOS AMBIENTES, A MEDIÇÃO FINAL SE DARÁ APÓS A CONCLUSÃO DA INSTALAÇÃO DOS MESMOS, OU INSTALAR APÓS A MONTAGEM DOS MÓVEIS.

**4-** SE HOUVER REDUÇÃO OU RECORTES NOS MÓDULOS, O CLIENTE TOMA CIÊNCIA QUE OS AJUSTES SERÃO EXECUTADOS NO LOCAL, QUE DEVE ESTAR LIVRE DE OBJETOS E PESSOAS QUE POSSAM SOFRER DE ALGUMA MANEIRA COM O PÓ DECORRENTE DESSES AJUSTES E QUALQUER OBJETO QUE NÃO POSSA SER RETIRADO DEVE ESTAR DEVIDAMENTE COBERTO. POR NÃO POSSUIR PROFISSIONÁIS ESPECIALIZADOS EM INSTALAÇÕES DE ELETROS, INSTALAÇÕES HIDRÁULICAS, A EMPRESA NÃO EFETUARÁ ESSE TIPO DE SERVIÇO. É NECESSÁRIO FORNECER AS PLANTAS DE INSTALAÇÃO ELÉTRICA E HIDRÁULICA DOS AMBIENTES NO DIA DA MONTAGEM, É NECESSÁRIO O ACOMPANHAMENTO DO CLIENTE OU UM RESPONSÁVEL PELA OBRA, MAIOR QUE 18 ANOS PARA TIRAR EVENTUAIS DÚVIDAS DOS MONTADORES REFERENTE AOS LOCAIS ONDE É POSSÍVEL FAZER FURAÇÕES. A ASSINATURA DESSE PROJETO SUBSTITUI QUALQUER PROJETO ANTERIOR.

**5-** O CLIENTE DECLARA ESTAR CIENTE QUE CASO O PROJETO ENVOLVA ELETROS, OS MESMOS DEVERÃO ESTAR NO LOCAL NO DIA DA MONTAGEM PARA ADEQUAÇÃO DOS NICHOS NECESSÁRIOS, E SE NÃO COMPROU OS ELETROS, SE RESPONSABILIZA EM ADQUIRIR OS MESMOS DENTRO DAS MEDIDAS ESPECIFICADAS NESTE PROJETO.

**6-** DECLARO ESTAR DE ACORDO COM ESTE PROJETO E COM AS MEDIDAS NELE DESCRITAS E CIENTE DE QUE NELE CONSTAM APENAS PEÇAS E MÓDULOS DA EMPRESA DUO PLANEJADOS, SENDO QUE OS DEMAIS ITENS SÃO MERAMENTE ILUSTRATIVOS (TAIS COMO ELETROS, COLCHÕES, GRANITOS E DECORAÇÕES EM GERAL).



CLIENTE: **PRISCILA**

AMBIENTE: **Cozinha**

PROJETISTA TÉCNICO: **JOÃO FELIPE SANTOS**

ARQUITETA: **FERNANDA**

**ATENÇÃO:**

DECLARO ESTAR DE ACORDO COM ESTE PROJETO E COM AS MEDIDAS NELE DESCRITAS E CIENTE DE QUE NELE CONSTAM APENAS PEÇAS E MÓDULOS DA EMPRESA, SENDO QUE OS DEMAIS ITENS SÃO MERAMENTE ILUSTRATIVOS (TAIS COMO ELETROS, COLCHÕES, GRANITOS E DECORAÇÕES NO GERAL).

ASS.: \_\_\_\_\_

**PRANCHA  
03**

## PLANTA - ESPECIFICAÇÕES DO PROJETO

### ESPECIFICAÇÕES DO PROJETO

#### CORES E ACABAMENTOS:

Caixa Módulos (Interno): **Branco, Nude, Freijo Puro**

Portas e Frentes: **Nude, Freijo Puro**

Tamponamentos: **Freijo Puro, Nude, Branco**

Painéis e Tapos: **Freijo Puro, Nude, Branco**

Puxadores: **Champagne**

Portas de Vidro: **Vidro Reflecta Bronze .. (Posição 1)**

#### FERRAGENS E ACESSÓRIOS:

Dobradiças:

**Dobradiça Reta c/ Amortecedor, Dobradiça Super Curva c/ Amortecedor**

Corrediças: **Gaveta Corrediça Telescópica**

Puxadores:

**Puxador Alumínio Cava Bronze - 196x55x18mm, Puxador Alumínio Cava Bronze - 236.499x55x18mm, Puxador Alumínio Cava Bronze - 386x55x18mm, Puxador Alumínio Cava Bronze - 387x55x18mm, Puxador Alumínio Cava Bronze - 461.5x55x18mm, Puxador Alumínio Cava Bronze - 496.5x55x18mm, Puxador Alumínio Cava Bronze - 834x55x18mm, Puxador Curvo Champagne · (Posição 4), Puxador Linear (15, 18 e 20mm) Pino Champagne - 200mm**

Ferragens especiais:

#### ESPESSURAS:


Caixa Módulos (Interno): **18mm e 25mm (fundo 6mm)**

Prateleiras internas: **18mm**

Portas e Frentes: **18mm**

Tamponamentos: **15mm e 18mm**

Painéis e Tapos e perfil: **6mm e 15mm e 18mm e 25mm**

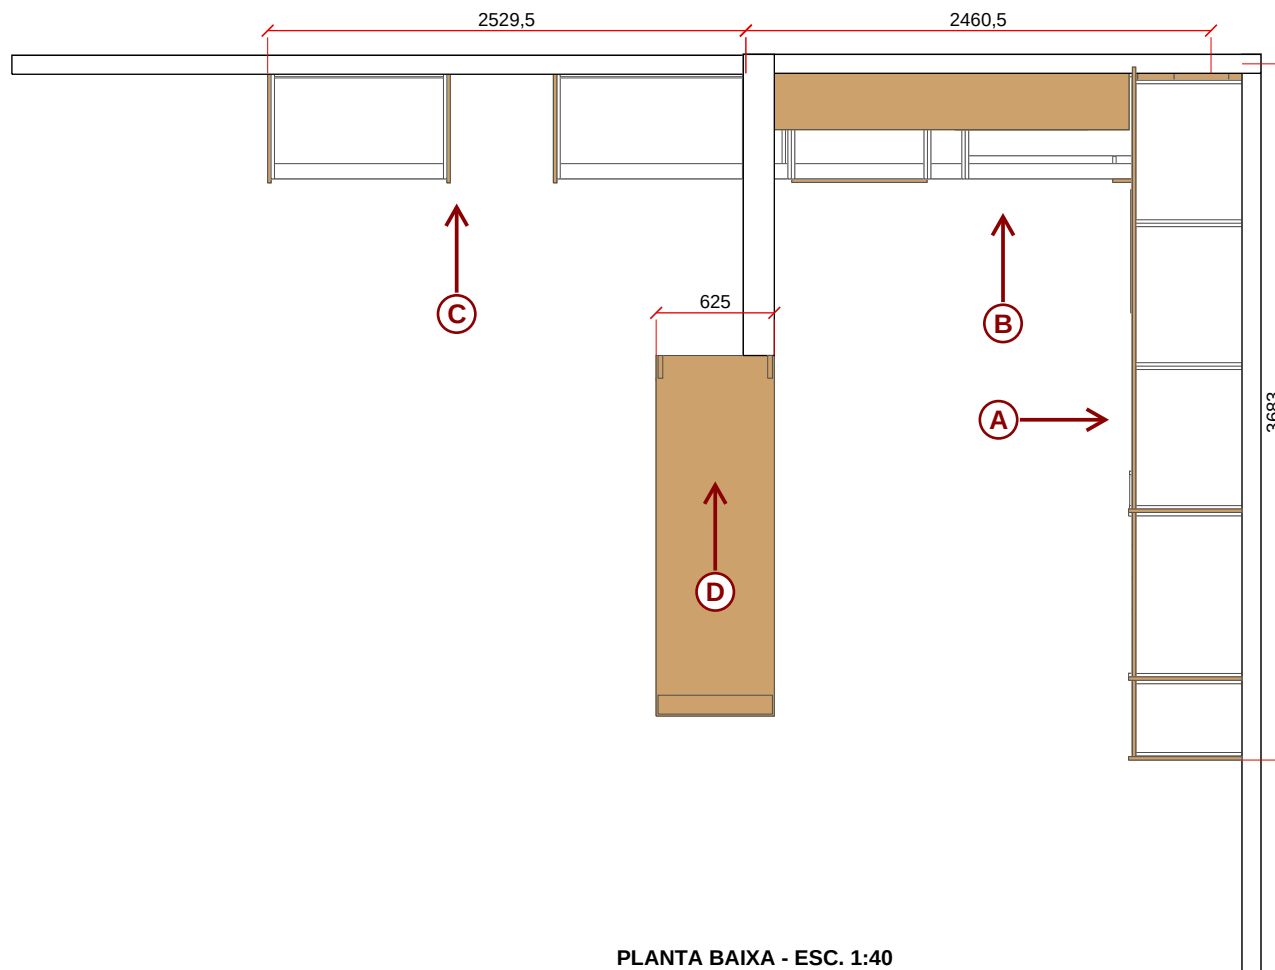

PLANTA BAIXA - ESC. 1:40



CLIENTE: **PRISCILA**

AMBIENTE: **Cozinha**

PROJETISTA TÉCNICO: **JOÃO FELIPE SANTOS**

ARQUITETA: **FERNANDA**

**ATENÇÃO:**

DECLARO ESTAR DE ACORDO COM ESTE PROJETO E COM AS MEDIDAS NELE DESCRITAS E CIENTE DE QUE NELE CONSTAM APENAS PEÇAS E MÓDULOS DA EMPRESA, SENDO QUE OS DEMAIS ITENS SÃO MERAMENTE ILUSTRATIVOS (TAIS COMO ELETROS, COLCHÕES, GRANITOS E DECORAÇÕES NO GERAL).

ASS.: \_\_\_\_\_

**PRANCHA  
04**

## **VISÃO GERAL DOS MÓVEIS**


**VISTA A**




**VISTA B**



**VISTA C**

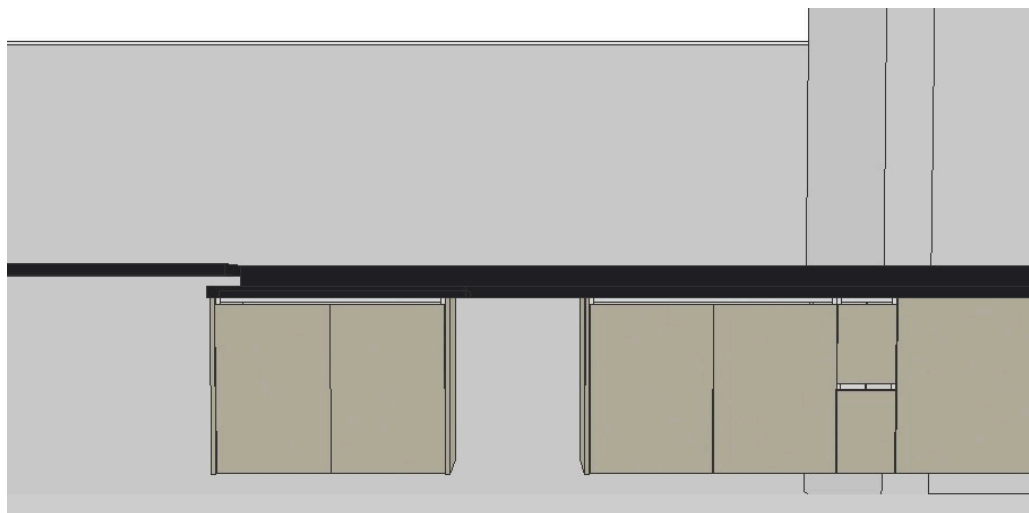

**PAINEL COM NICHOS**

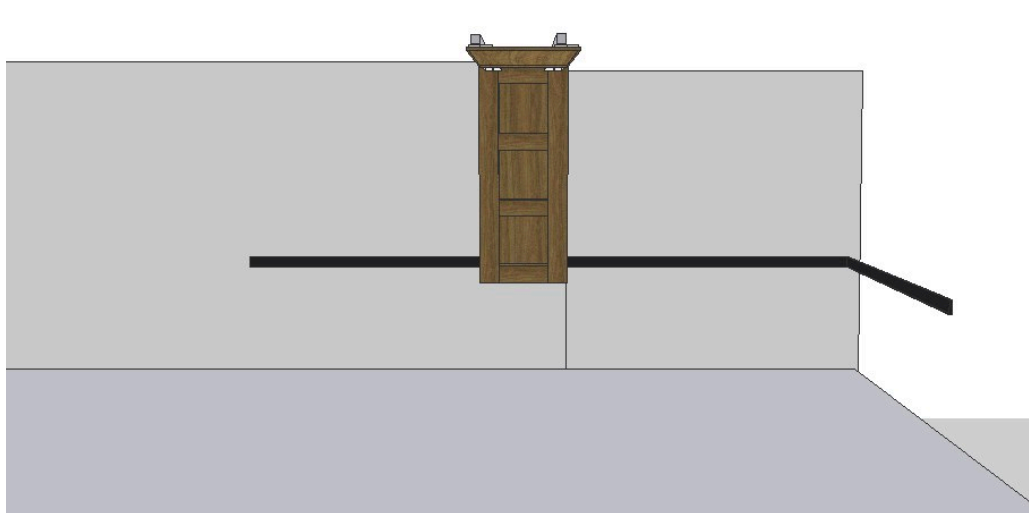



CLIENTE: **PRISCILA**

AMBIENTE: **Cozinha**

PROJETISTA TÉCNICO: **JOÃO FELIPE SANTOS**

ARQUITETA: **FERNANDA**

**ATENÇÃO:**

DECLARO ESTAR DE ACORDO COM ESTE PROJETO E COM AS MEDIDAS NELE DESCRITAS E CIENTE DE QUE NELE CONSTAM APENAS PEÇAS E MÓDULOS DA EMPRESA, SENDO QUE OS DEMAIS ITENS SÃO MERAMENTE ILUSTRATIVOS (TAIS COMO ELETROS, COLCHÕES, GRANITOS E DECORAÇÕES NO GERAL).

ASS.: \_\_\_\_\_

**PRANCHA  
05**

## MÓDULOS E PAINÉIS - VISTA A



| Item | Descrição                         | Dimensão     |
|------|-----------------------------------|--------------|
| 1    | Armário Despenseiro               | 400x2390x580 |
| 2    | Armário Superior                  | 756x586x580  |
| 3    | Armário Superior                  | 870x490x580  |
| 4    | Armário Superior                  | 950x400x430  |
| 5    | Balcão Inferior                   | 200x714x595  |
| 6    | Balcão Inferior                   | 838x714x570  |
| 7    | Armário Adega/Nicho               | 150x870x600  |
| 8    | Balcão 2 Portas                   | 650x714x570  |
| 9    | Painel Branco MDF                 | 100x15x266   |
| 10   | Painel Branco MDF                 | 266x15x150   |
| 11   | Painel Freijo Puro MDF            | 320x15x120   |
| 12   | Painel Freijo Puro MDF            | 320x15x200   |
| 13   | Painel Freijo Puro MDF            | 1286x15x400  |
| 14   | Painel Freijo Puro MDF            | 404x18x97    |
| 15   | Painel Freijo Puro MDF            | 400x18x70    |
| 16   | Painel Freijo Puro MDF            | 436x18x450   |
| 17   | Painel Freijo Puro MDF            | 2337x18x450  |
| 18   | Painel Freijo Puro MDF            | 400x18x450   |
| 19   | Painel Nude MDP                   | 2487x18x600  |
| 20   | Painel Nude MDP                   | 700x18x650   |
| 21   | Painel Nude MDP                   | 870x18x97    |
| 22   | Painel Nude MDP                   | 2338x18x97   |
| 23   | Painel Nude MDP                   | 586x18x70    |
| 24   | Tamponamento Inferior             | 2305x18x70   |
| 25   | Tamponamento Inferior             | 2355x18x220  |
| 26*  | QUADRO EM C SUPERIOR 20 X 20 X 20 | 20x1024x318  |
| 27*  | SUPORTE FIXAÇÃO METALON 36 X 18 P | 36x2x18      |
| 28*  | Cunha 45° 25MM                    | 2700x25x70   |

\* não localizado no DXF - conferir

### DETALHE - NICHO



### DETALHE - NICHO

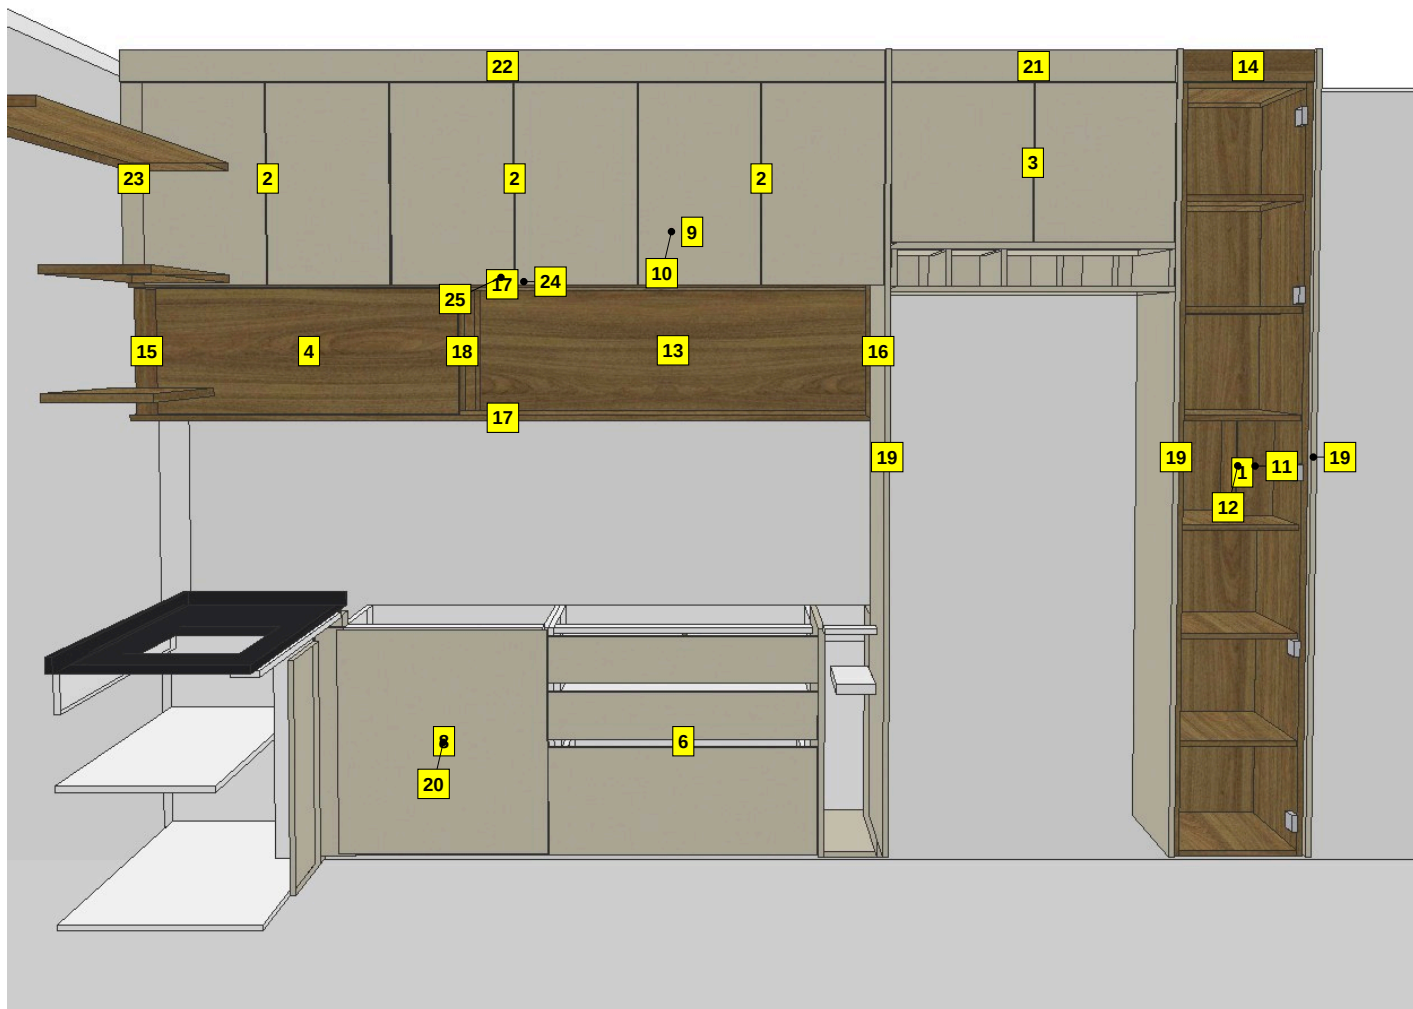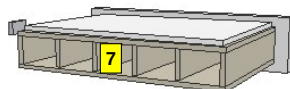



CLIENTE: **PRISCILA**

AMBIENTE: **Cozinha**

PROJETISTA TÉCNICO: **JOÃO FELIPE SANTOS**

ARQUITETA: **FERNANDA**

**ATENÇÃO:**


DECLARO ESTAR DE ACORDO COM ESTE PROJETO E COM AS MEDIDAS NELE DESCRITAS E CIENTE DE QUE NELE CONSTAM APENAS PEÇAS E MÓDULOS DA EMPRESA, SENDO QUE OS DE MAIS ITENS SÃO MERAMENTE ILUSTRATIVOS (TAIS COMO ELETROS, COLCHÕES, GRANITOS E DECORAÇÕES NO GERAL).

ASS.: \_\_\_\_\_

**PRANCHA  
06**

## MÓDULOS E PAINÉIS - VISTA B

| Item | Descrição              | Dimensão      |
|------|------------------------|---------------|
| 1    | Balcão Inferior        | 1300x714x559  |
| 2    | Balcão Inferior        | 200x714x559   |
| 3    | Balcão Inferior        | 240,5x714x559 |
| 4    | Balcão Inferior        | 720x714x559   |
| 5    | Painel Branco MDP      | 677,5x18x120  |
| 6    | Painel Branco MDP      | 1264x18x436   |
| 7    | Painel Freijo Puro MDF | 700x25x298    |
| 8    | Painel Freijo Puro MDF | 919x25x298    |
| 9    | Painel Freijo Puro MDF | 1876x25x298   |
| 10   | Painel Nude MDP        | 714x18x520    |
| 11   | Painel Nude MDP        | 709x18x715    |
| 12   | Painel Nude MDP        | 714x18x120    |

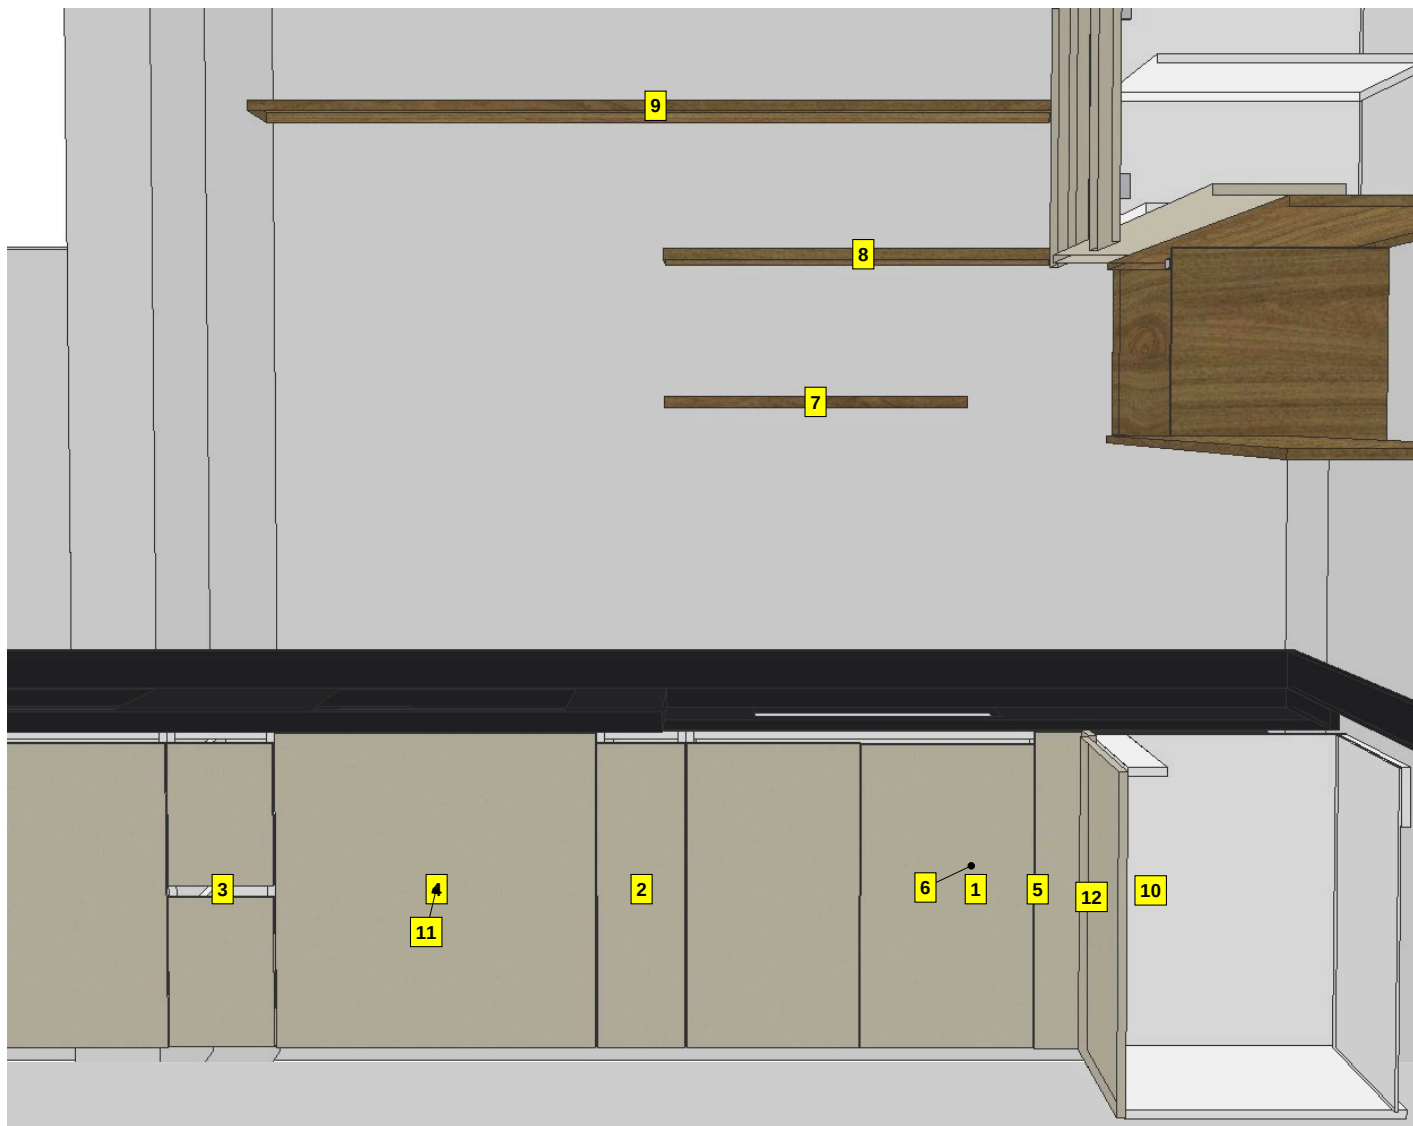

**VISTA B - ESC. 1:40**



CLIENTE: **PRISCILA**

AMBIENTE: **Cozinha**

PROJETISTA TÉCNICO: **JOÃO FELIPE SANTOS**

ARQUITETA: **FERNANDA**

**ATENÇÃO:**


DECLARO ESTAR DE ACORDO COM ESTE PROJETO E COM AS MEDIDAS NELE DESCRITAS E CIENTE DE QUE NELE CONSTAM APENAS PEÇAS E MÓDULOS DA EMPRESA, SENDO QUE OS DE MAIS ITENS SÃO MERAMENTE ILUSTRATIVOS (TAIS COMO ELETROS, COLCHÕES, GRANITOS E DECORAÇÕES NO GERAL).

ASS.: \_\_\_\_\_

**PRANCHA  
08**

## MÓDULOS E PAINÉIS - VISTA C

| Item | Descrição             | Dimensão     |
|------|-----------------------|--------------|
| 1    | Balcão Inferior       | 1000x714x559 |
| 2    | Balcão Inferior       | 930x714x559  |
| 3    | Tamponamento Inferior | 714x18x579   |

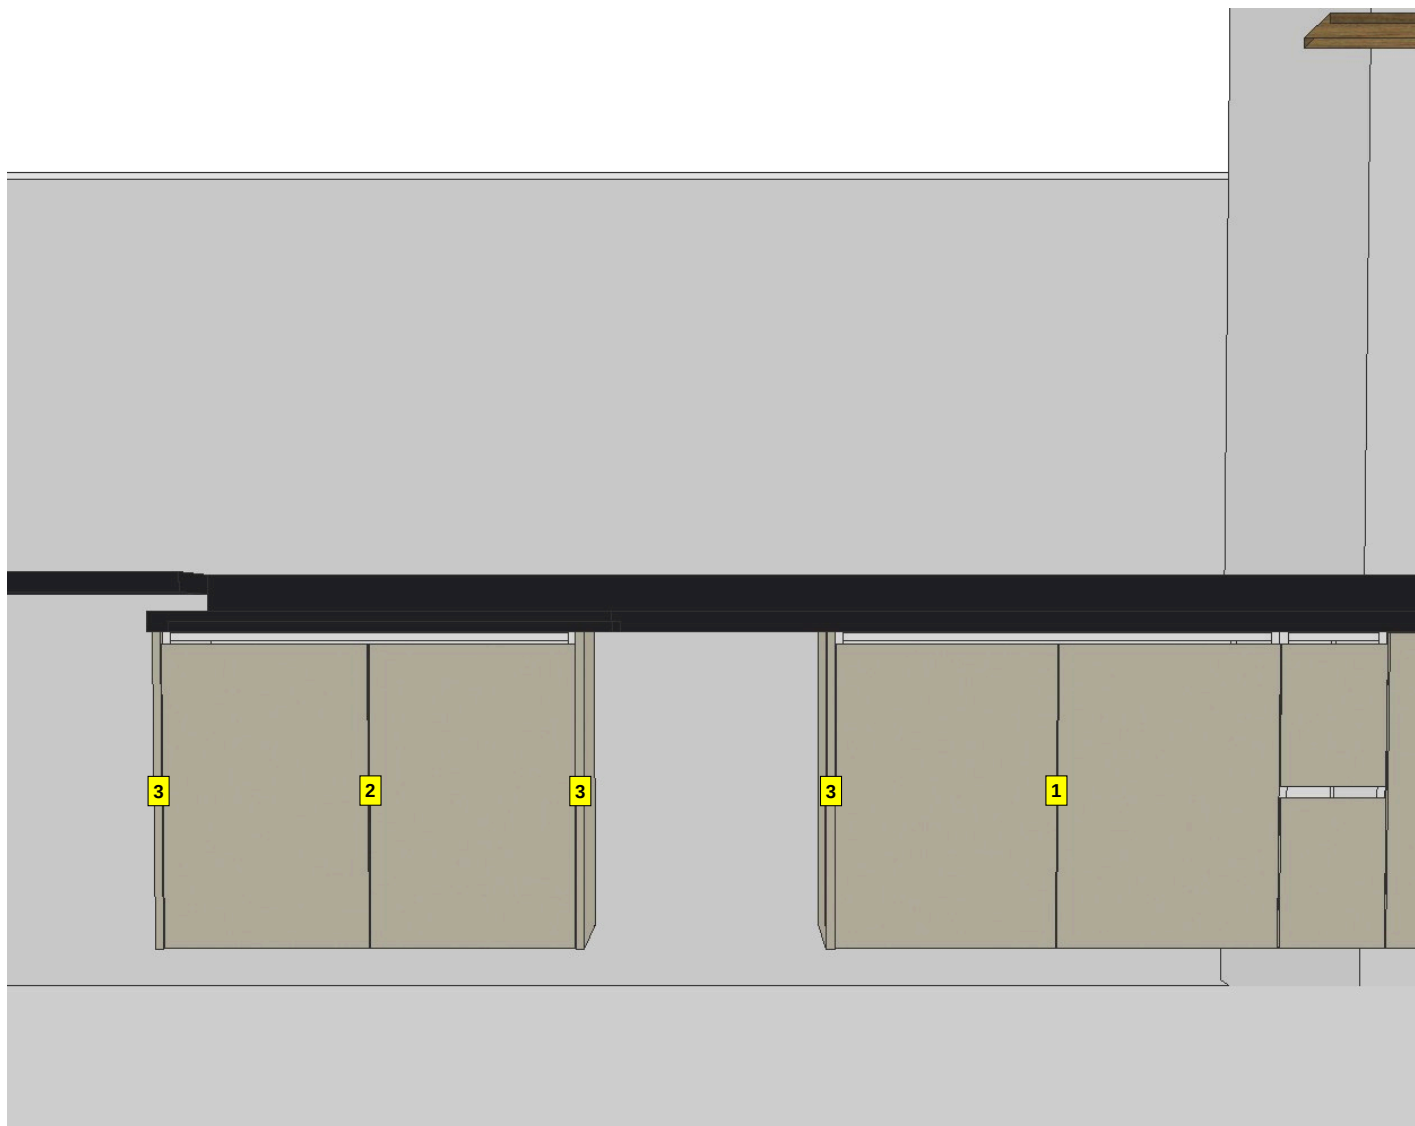





CLIENTE: **PRISCILA**

AMBIENTE: **Cozinha**

PROJETISTA TÉCNICO: **JOÃO FELIPE SANTOS**

ARQUITETA: **FERNANDA**

**ATENÇÃO:**

DECLARO ESTAR DE ACORDO COM ESTE PROJETO E COM AS MEDIDAS NELE DESCRITAS E CIENTE DE QUE NELE CONSTAM APENAS PEÇAS E MÓDULOS DA EMPRESA, SENDO QUE OS DEMAIS ITENS SÃO MERAMENTE ILUSTRATIVOS (TAIS COMO ELETROS, COLCHÕES, GRANITOS E DECORAÇÕES NO GERAL).

ASS.: \_\_\_\_\_

# PRANCHA 10

## MÓDULOS E PAINÉIS - PAINEL COM NICHOS

| Item | Descrição              | Dimensão    |
|------|------------------------|-------------|
| 1    | Painel Freijo Puro MDF | 1320x6x380  |
| 2    | Painel Freijo Puro MDF | 1530x15x625 |
| 3    | Painel Freijo Puro MDF | 1580x25x120 |
| 4    | Painel Freijo Puro MDF | 1907x15x625 |
| 5    | Painel Freijo Puro MDF | 605x25x100  |
| 6    | Tamponamento Inferior  | 350x15x90   |
| 7    | Tamponamento Inferior  | 1320x15x90  |





CLIENTE: **PRISCILA**

AMBIENTE: **Cozinha**

PROJETISTA TÉCNICO: **JOÃO FELIPE SANTOS**

ARQUITETA: **FERNANDA**

**ATENÇÃO:**


DECLARO ESTAR DE ACORDO COM ESTE PROJETO E COM AS MEDIDAS NELE DESCRITAS E CIENTE DE QUE NELE CONSTAM APENAS PEÇAS E MÓDULOS DA EMPRESA, SENDO QUE OS DEMAIS ITENS SÃO MERAMENTE ILUSTRATIVOS (TAIS COMO ELETROS, COLCHÕES, GRANITOS E DECORAÇÕES NO GERAL).

ASS.: \_\_\_\_\_

# PRANCHA 11

## MÓDULOS E PAINÉIS - PAINEL COM NICHOS

| Item | Descrição              | Dimensão    |
|------|------------------------|-------------|
| 1    | Painel Freijo Puro MDF | 1530x15x625 |
| 2    | Painel Freijo Puro MDF | 1580x25x120 |
| 3    | Painel Freijo Puro MDF | 1907x15x625 |
| 4    | Painel Freijo Puro MDF | 605x25x100  |
| 5    | Tamponamento Inferior  | 1320x15x90  |

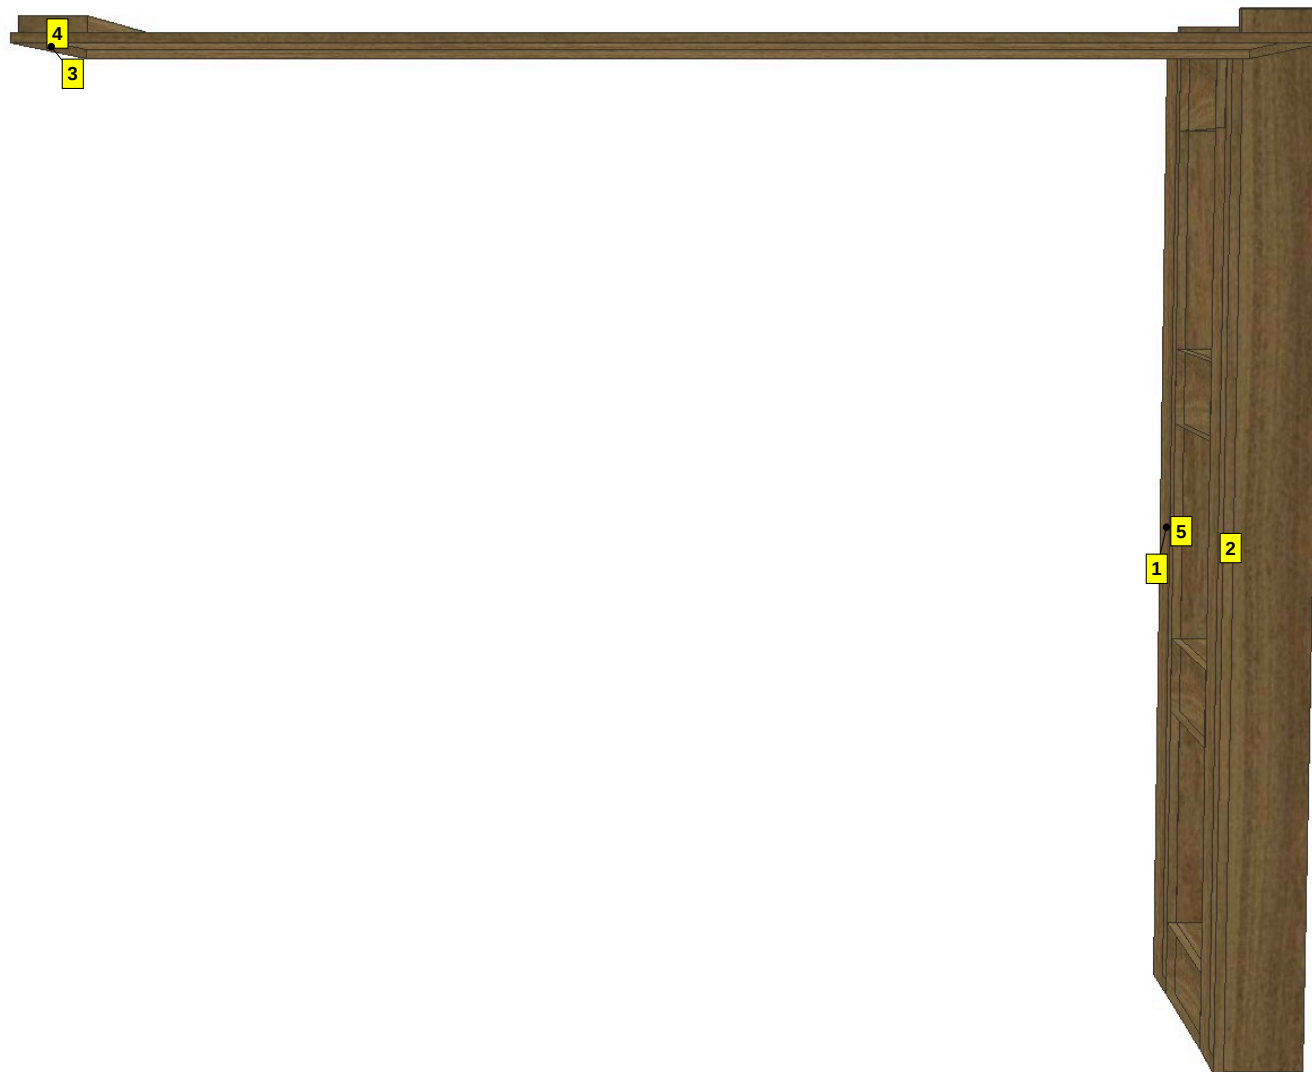



CLIENTE: **PRISCILA**

AMBIENTE: **Cozinha**

PROJETISTA TÉCNICO: **JOÃO FELIPE SANTOS**

ARQUITETA: **FERNANDA**


**ATENÇÃO:**

DECLARO ESTAR DE ACORDO COM ESTE PROJETO E COM AS MEDIDAS NELE DESCRITAS E CIENTE DE QUE NELE CONSTAM APENAS PEÇAS E MÓDULOS DA EMPRESA, SENDO QUE OS DEMAIS ITENS SÃO MERAMENTE ILUSTRATIVOS (TAIS COMO ELETROS, COLCHÕES, GRANITOS E DECORAÇÕES NO GERAL).


ASS.: \_\_\_\_\_

# PRANCHA 12

## MEDIDAS E ALTURAS - PAINEL COM NICHOS

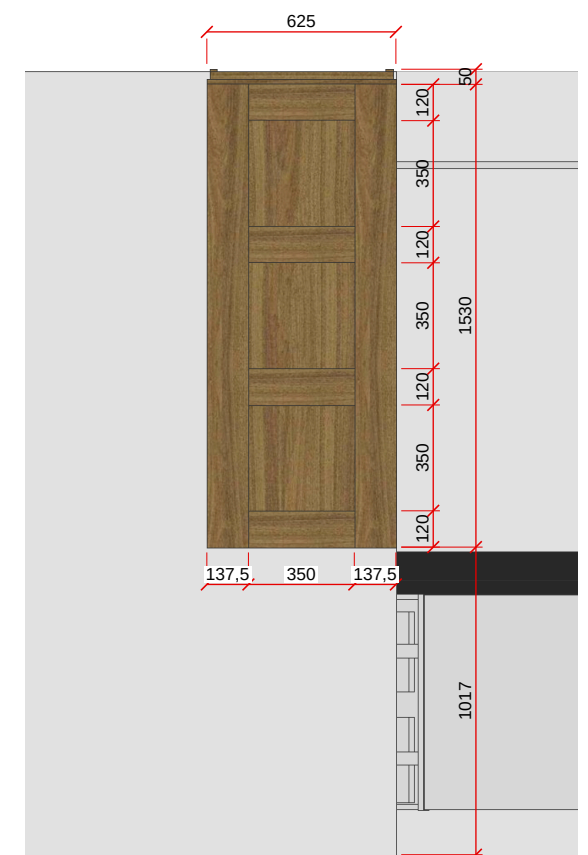

PAINEL COM NICHOS - ESC. 1:25

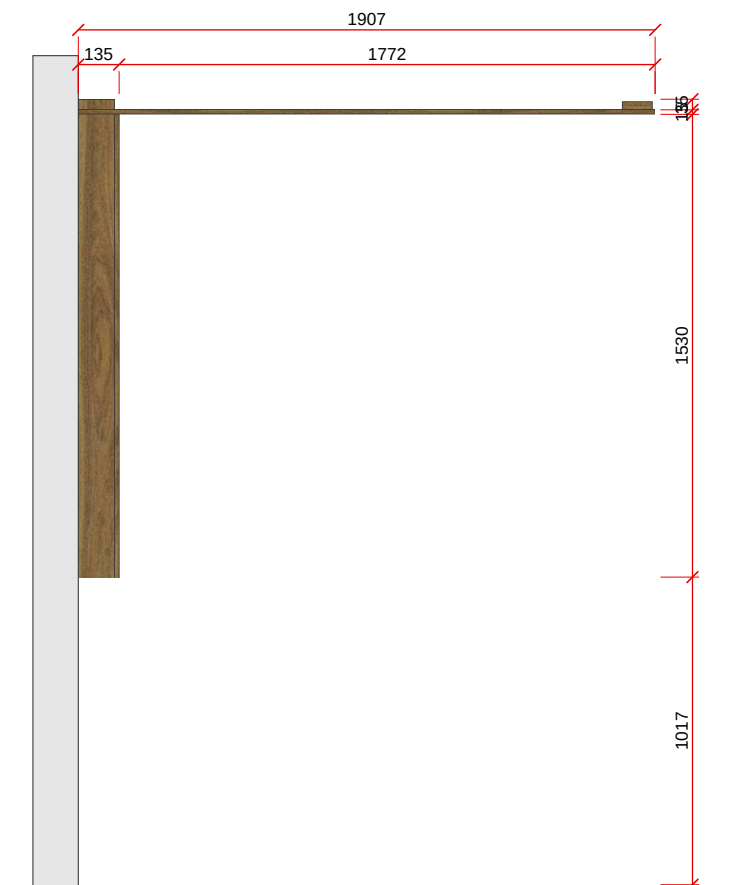

PAINEL COM NICHOS - LATERAL - ESC. 1:25



CLIENTE: **PRISCILA**

AMBIENTE: **Cozinha**

PROJETISTA TÉCNICO: **JOÃO FELIPE SANTOS**

ARQUITETA: **FERNANDA**



**ATENÇÃO:**  
DECLARO ESTAR DE ACORDO COM ESTE PROJETO E COM AS MEDIDAS NELE DESCRITAS E CIENTE DE QUE NELE CONSTAM APENAS PEÇAS E MÓDULOS DA EMPRESA , SENDO QUE OS DEMAIS ITENS SÃO MERAMENTE ILUSTRATIVOS (TAIS COMO ELETROS, COLCHÕES, GRANITOS E DECORAÇÕES NO GERAL).

ASS.: \_\_\_\_\_

**PRANCHA**  
**13**

**DIVISOR DE GAVETA**

| Item | Descrição              | Dimensão  |
|------|------------------------|-----------|
| 1    | Painel Freijo Puro MDF | 708x15x70 |
| 2    | Painel Freijo Puro MDF | 297x15x70 |
| 3    | Painel Freijo Puro MDF | 462x15x70 |

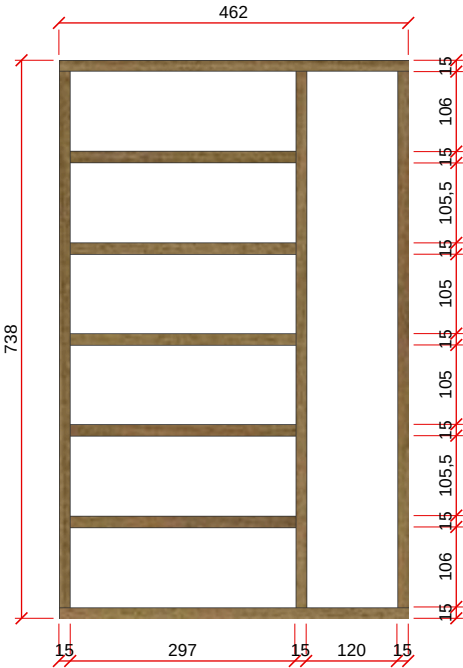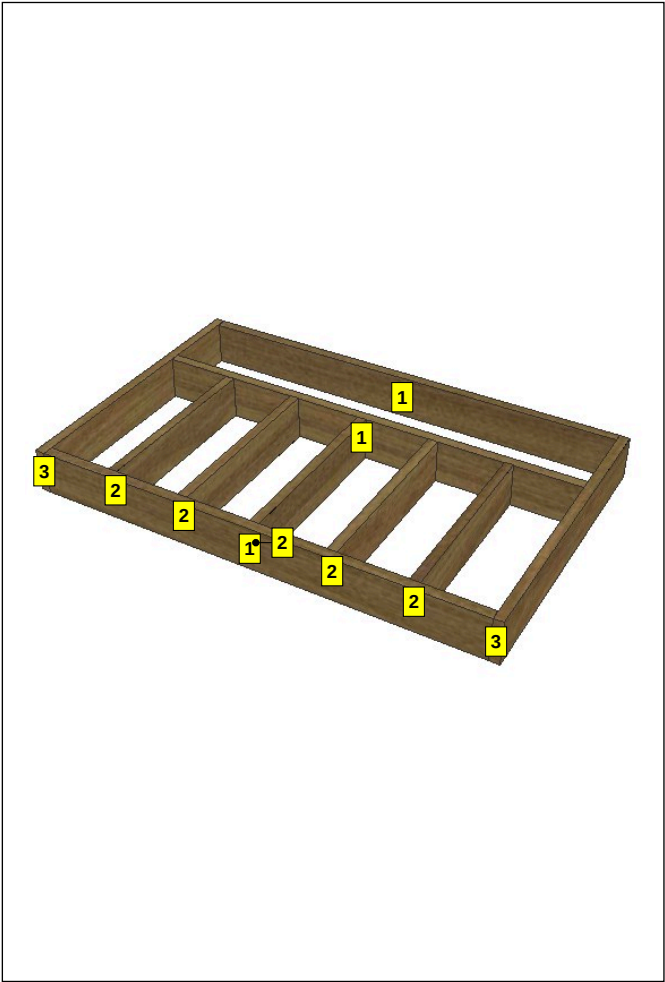

DIVISOR - VISTA DE CIMA - ESC. 1:10 | ALTURA: 70 mm